






Planos Anexos

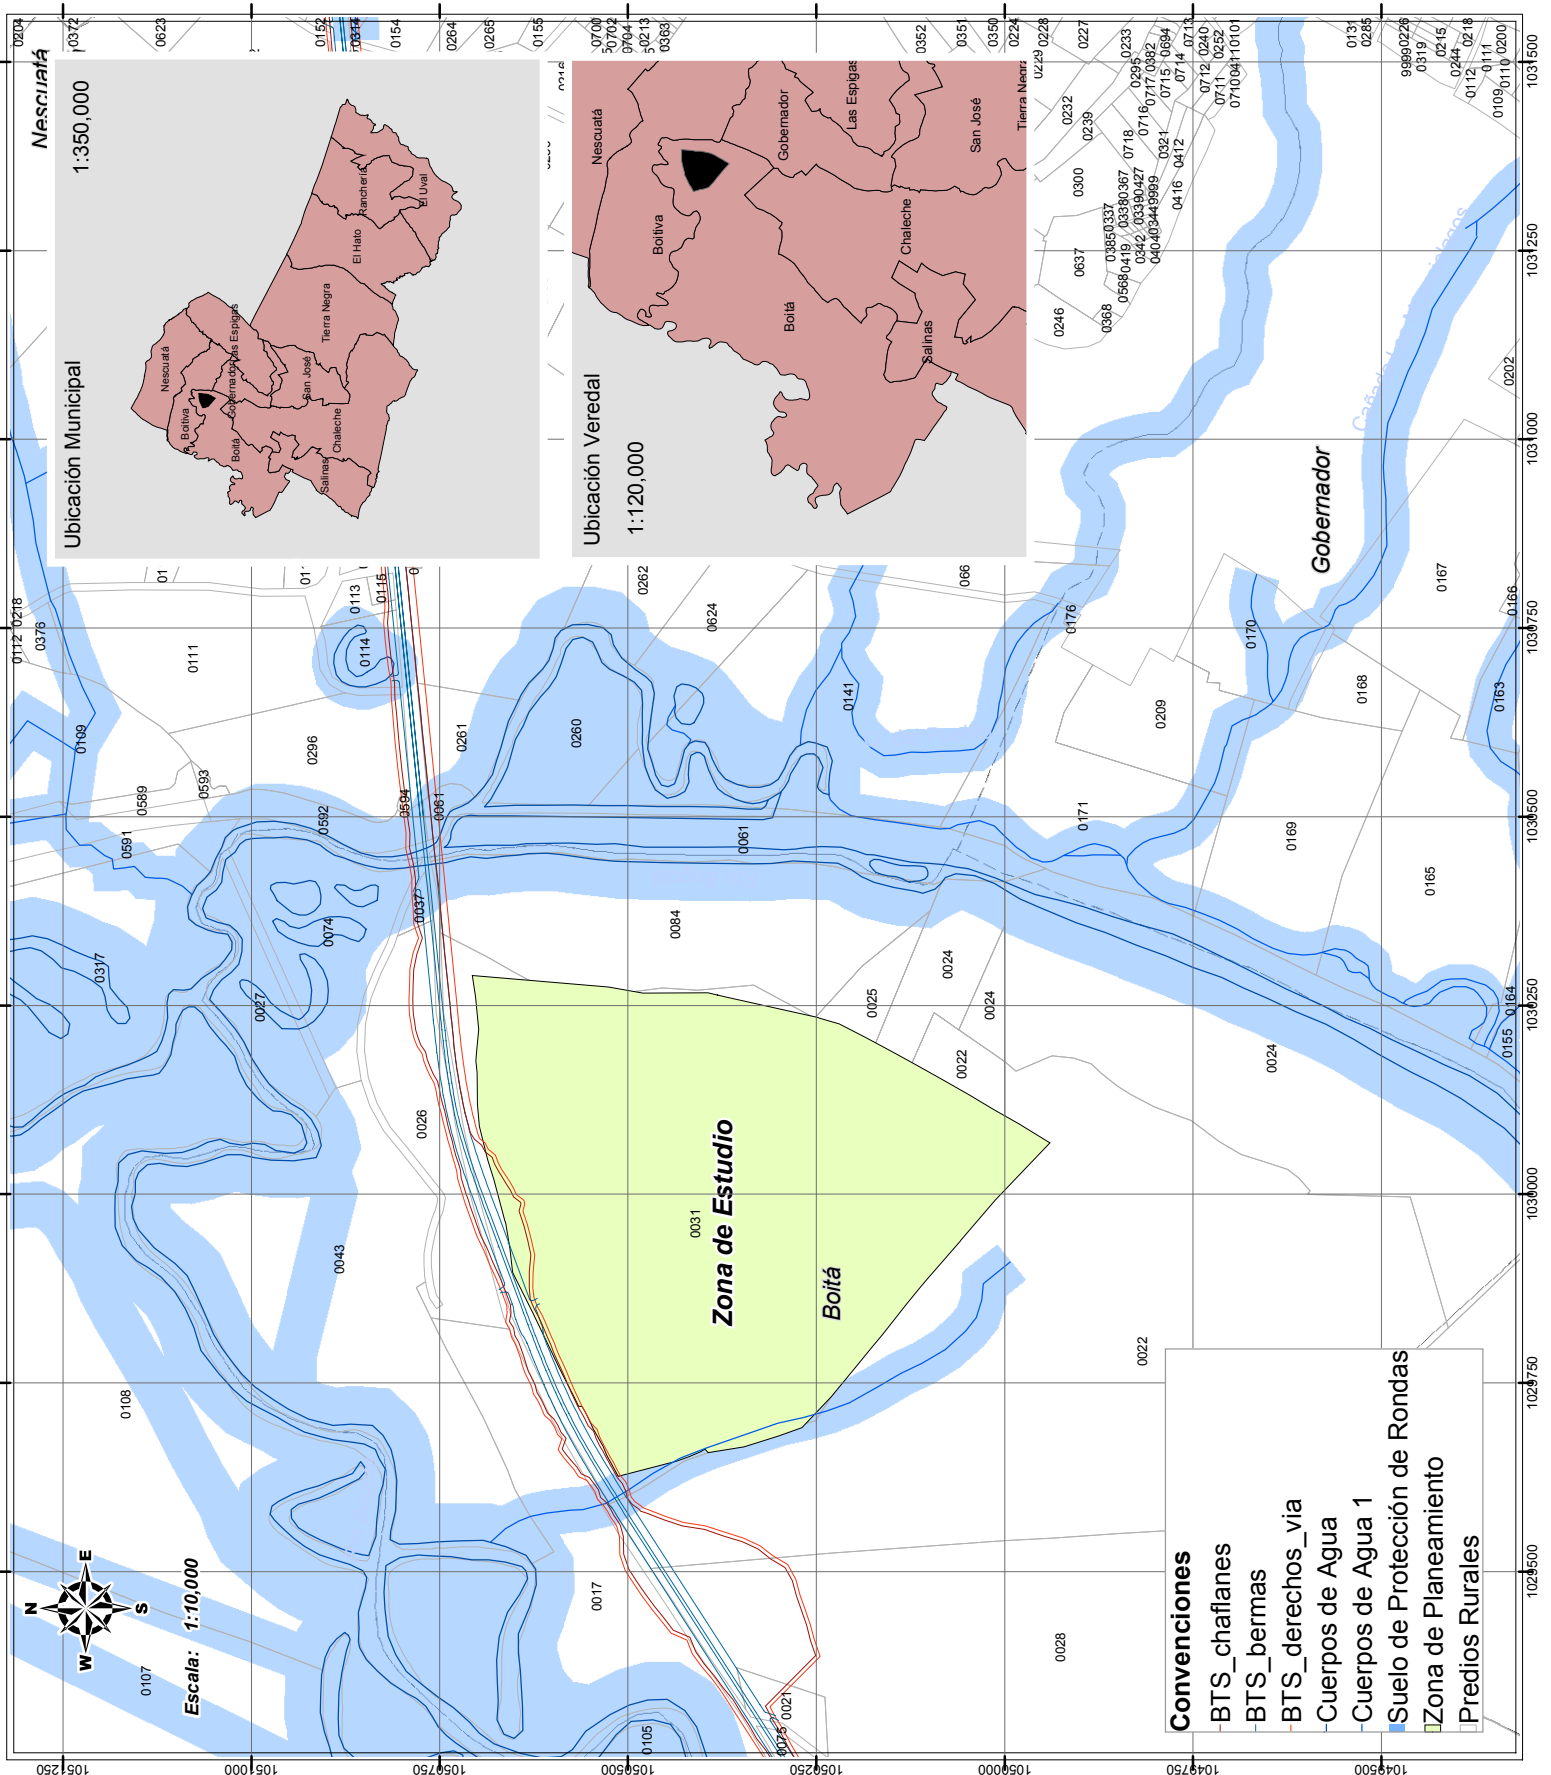


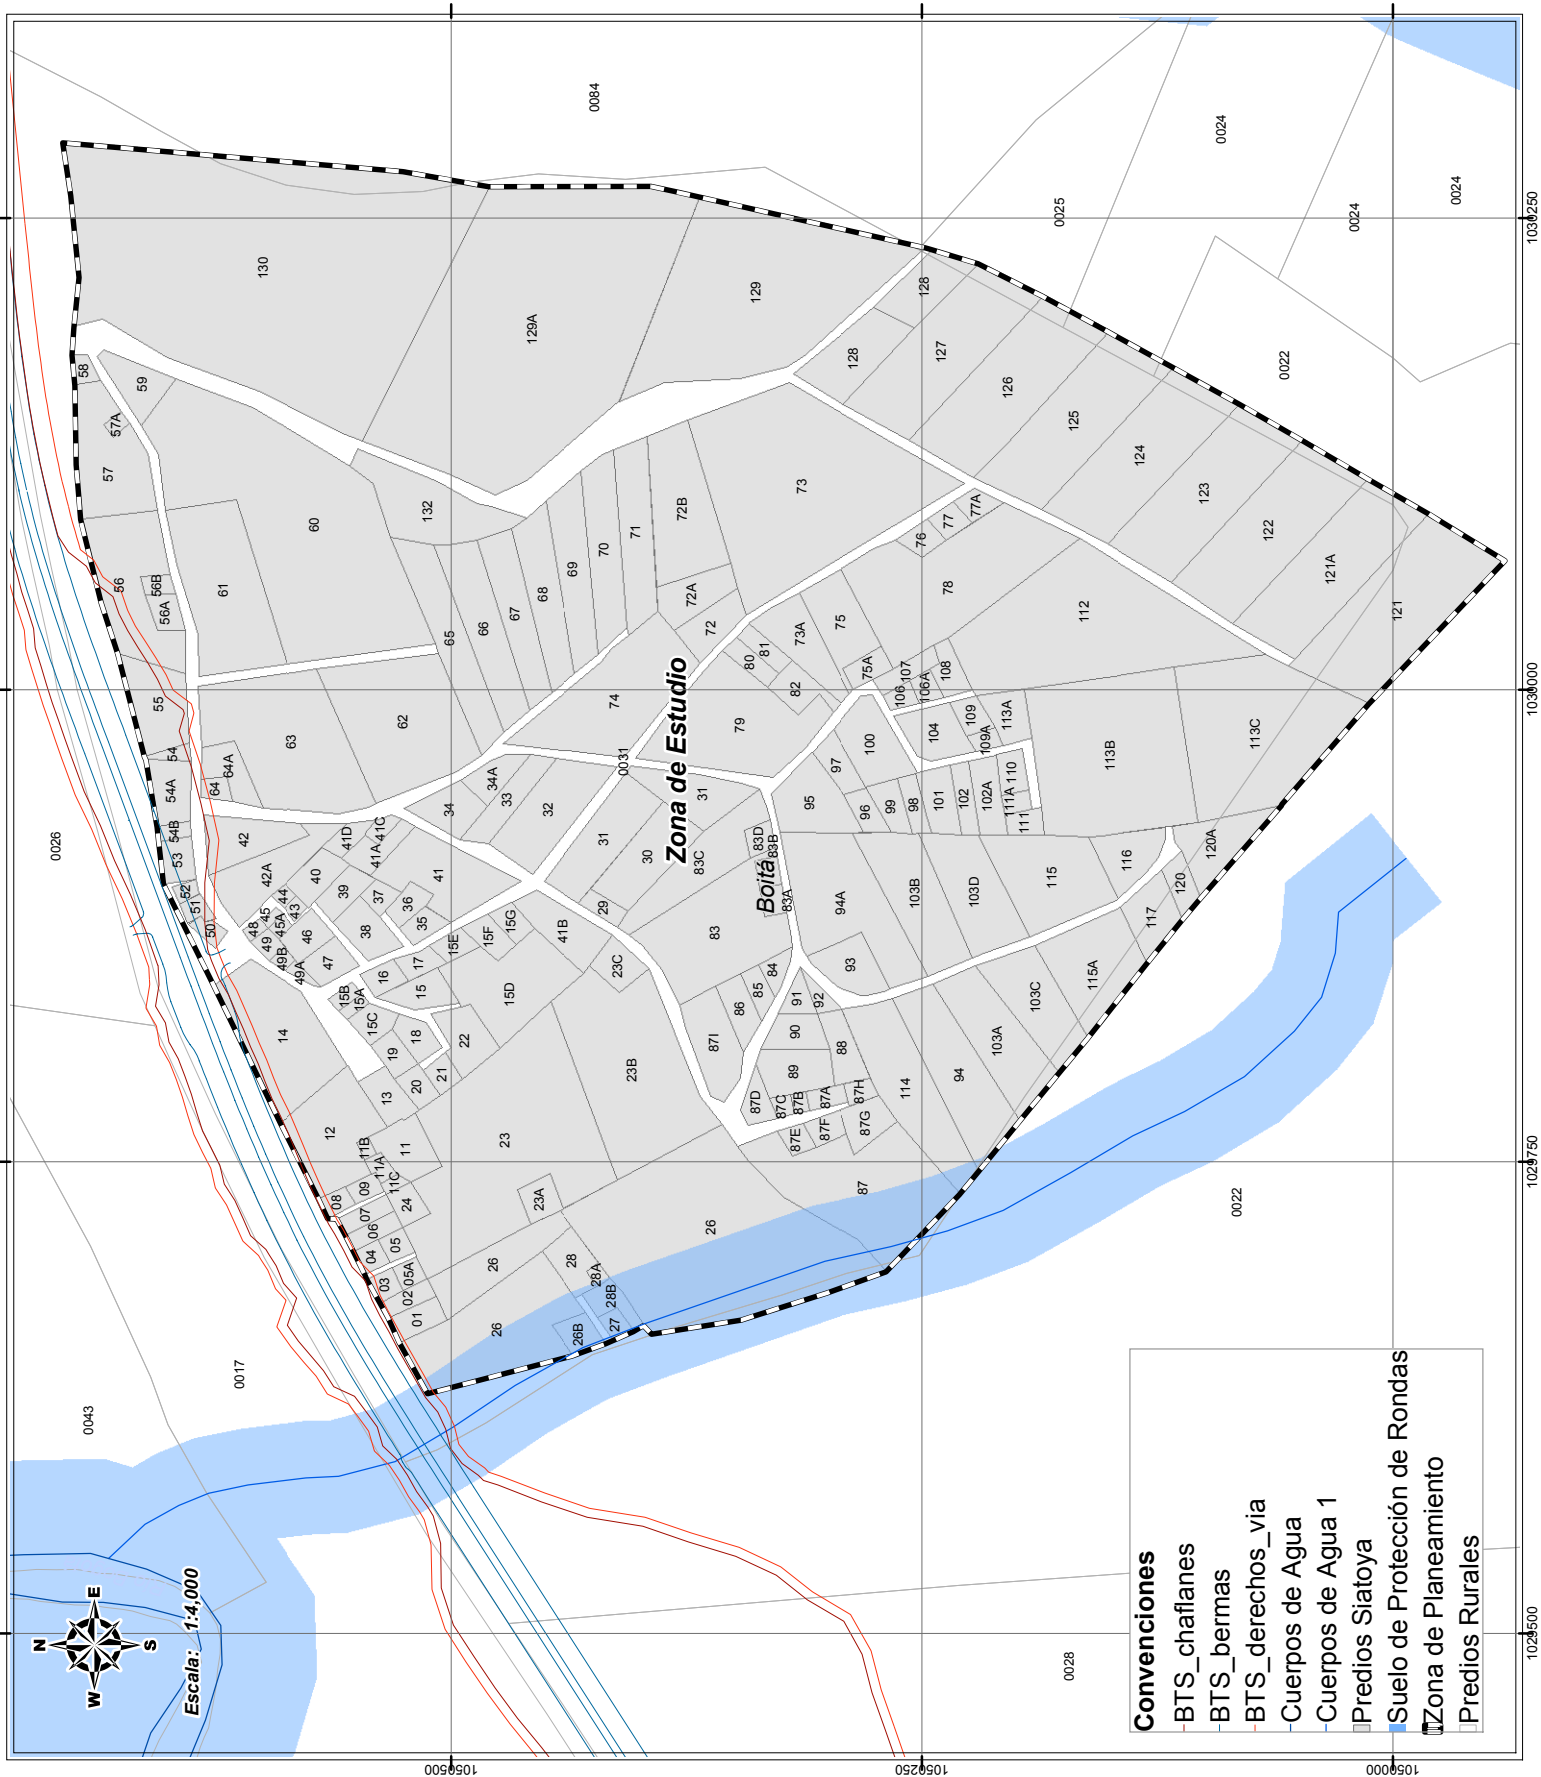

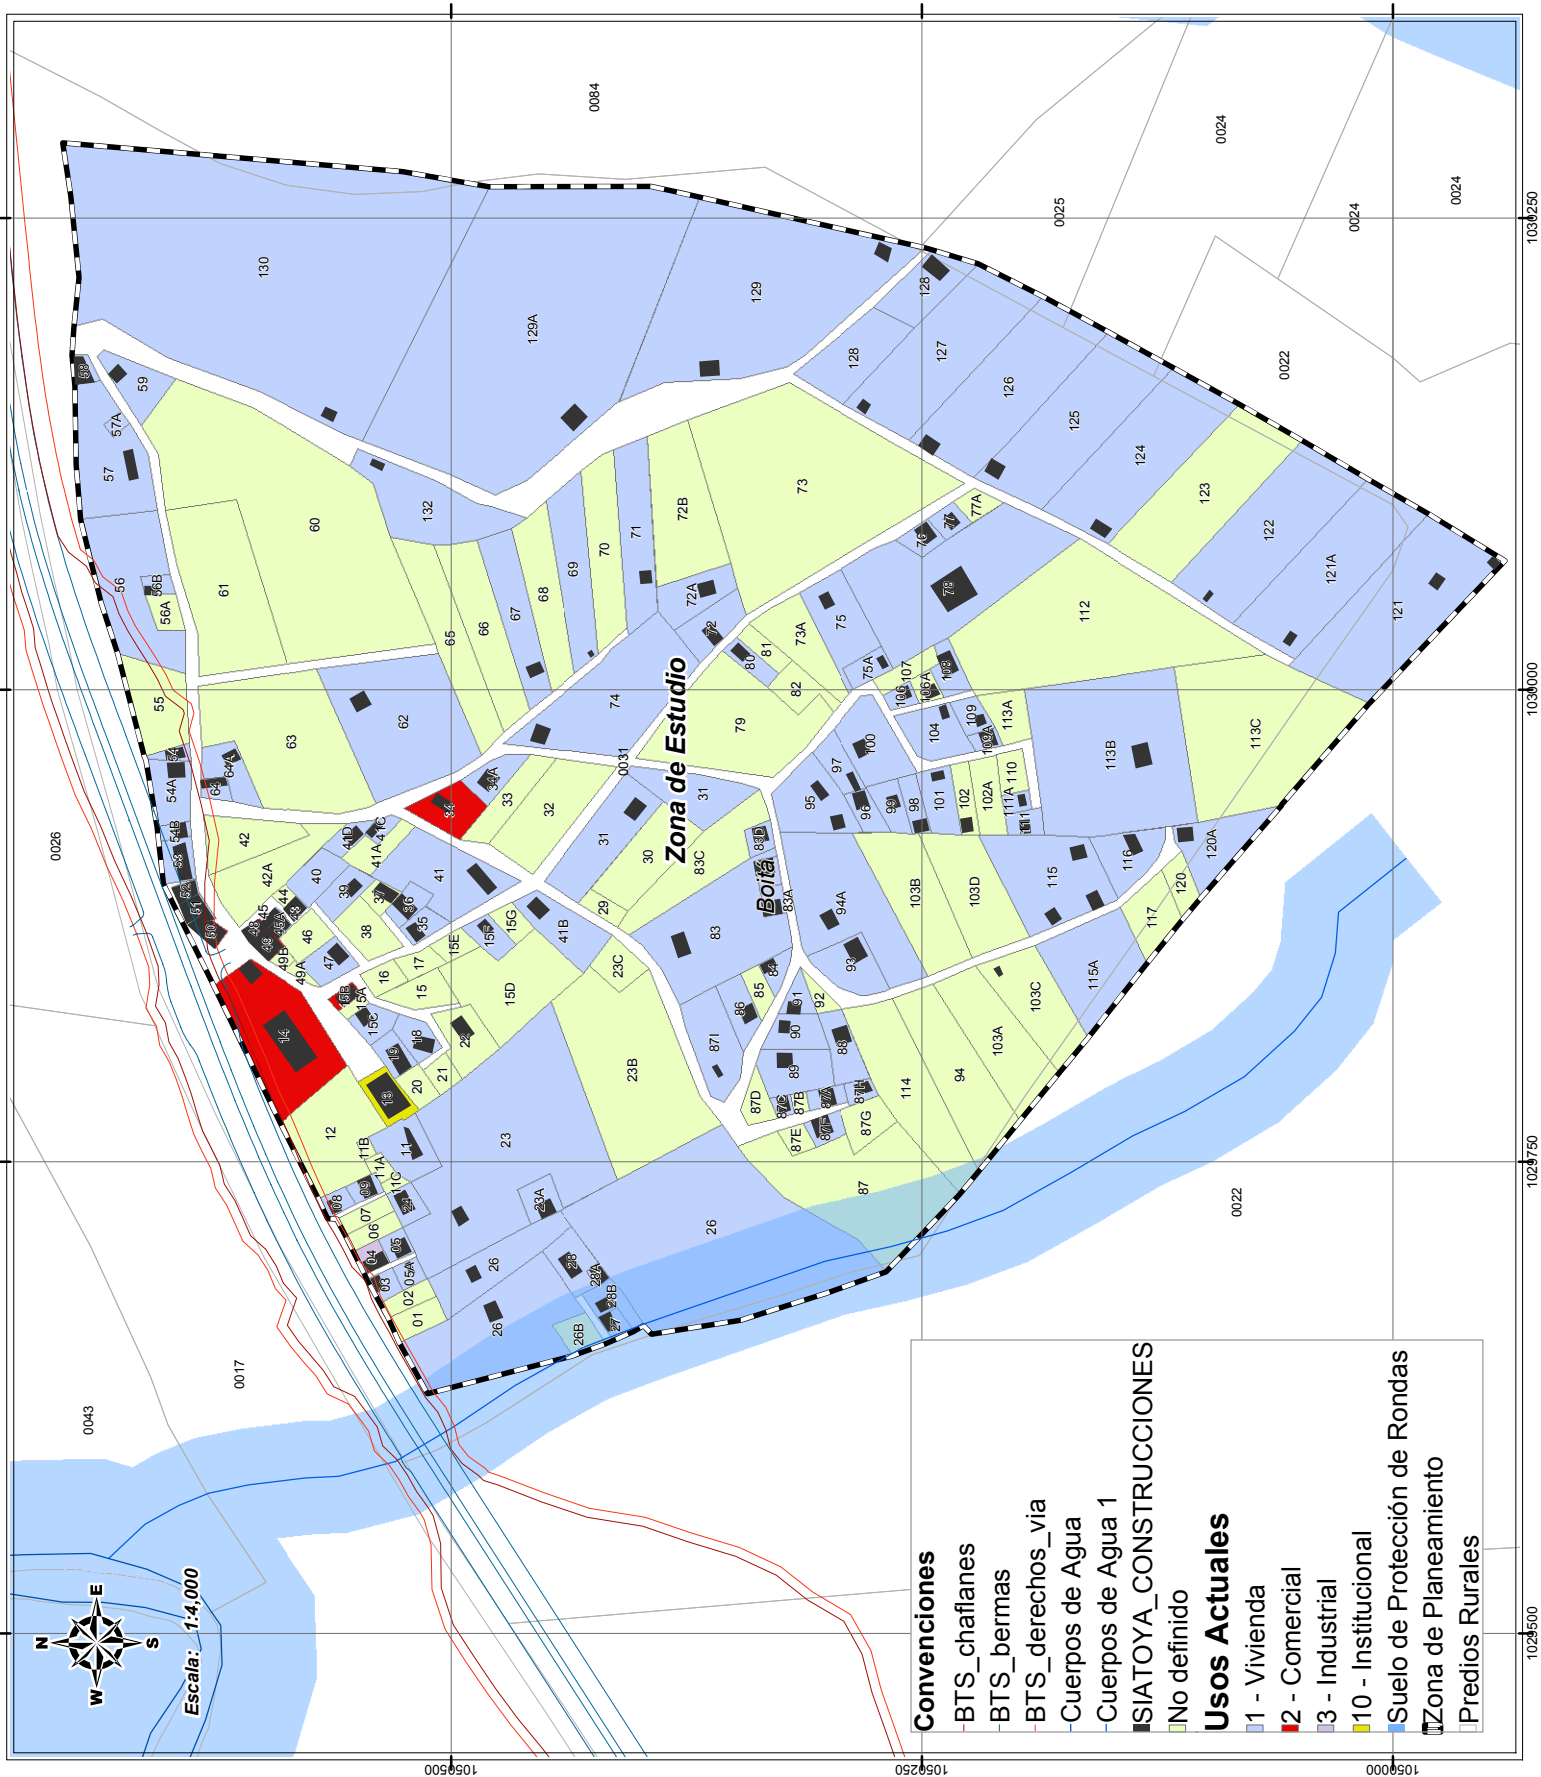

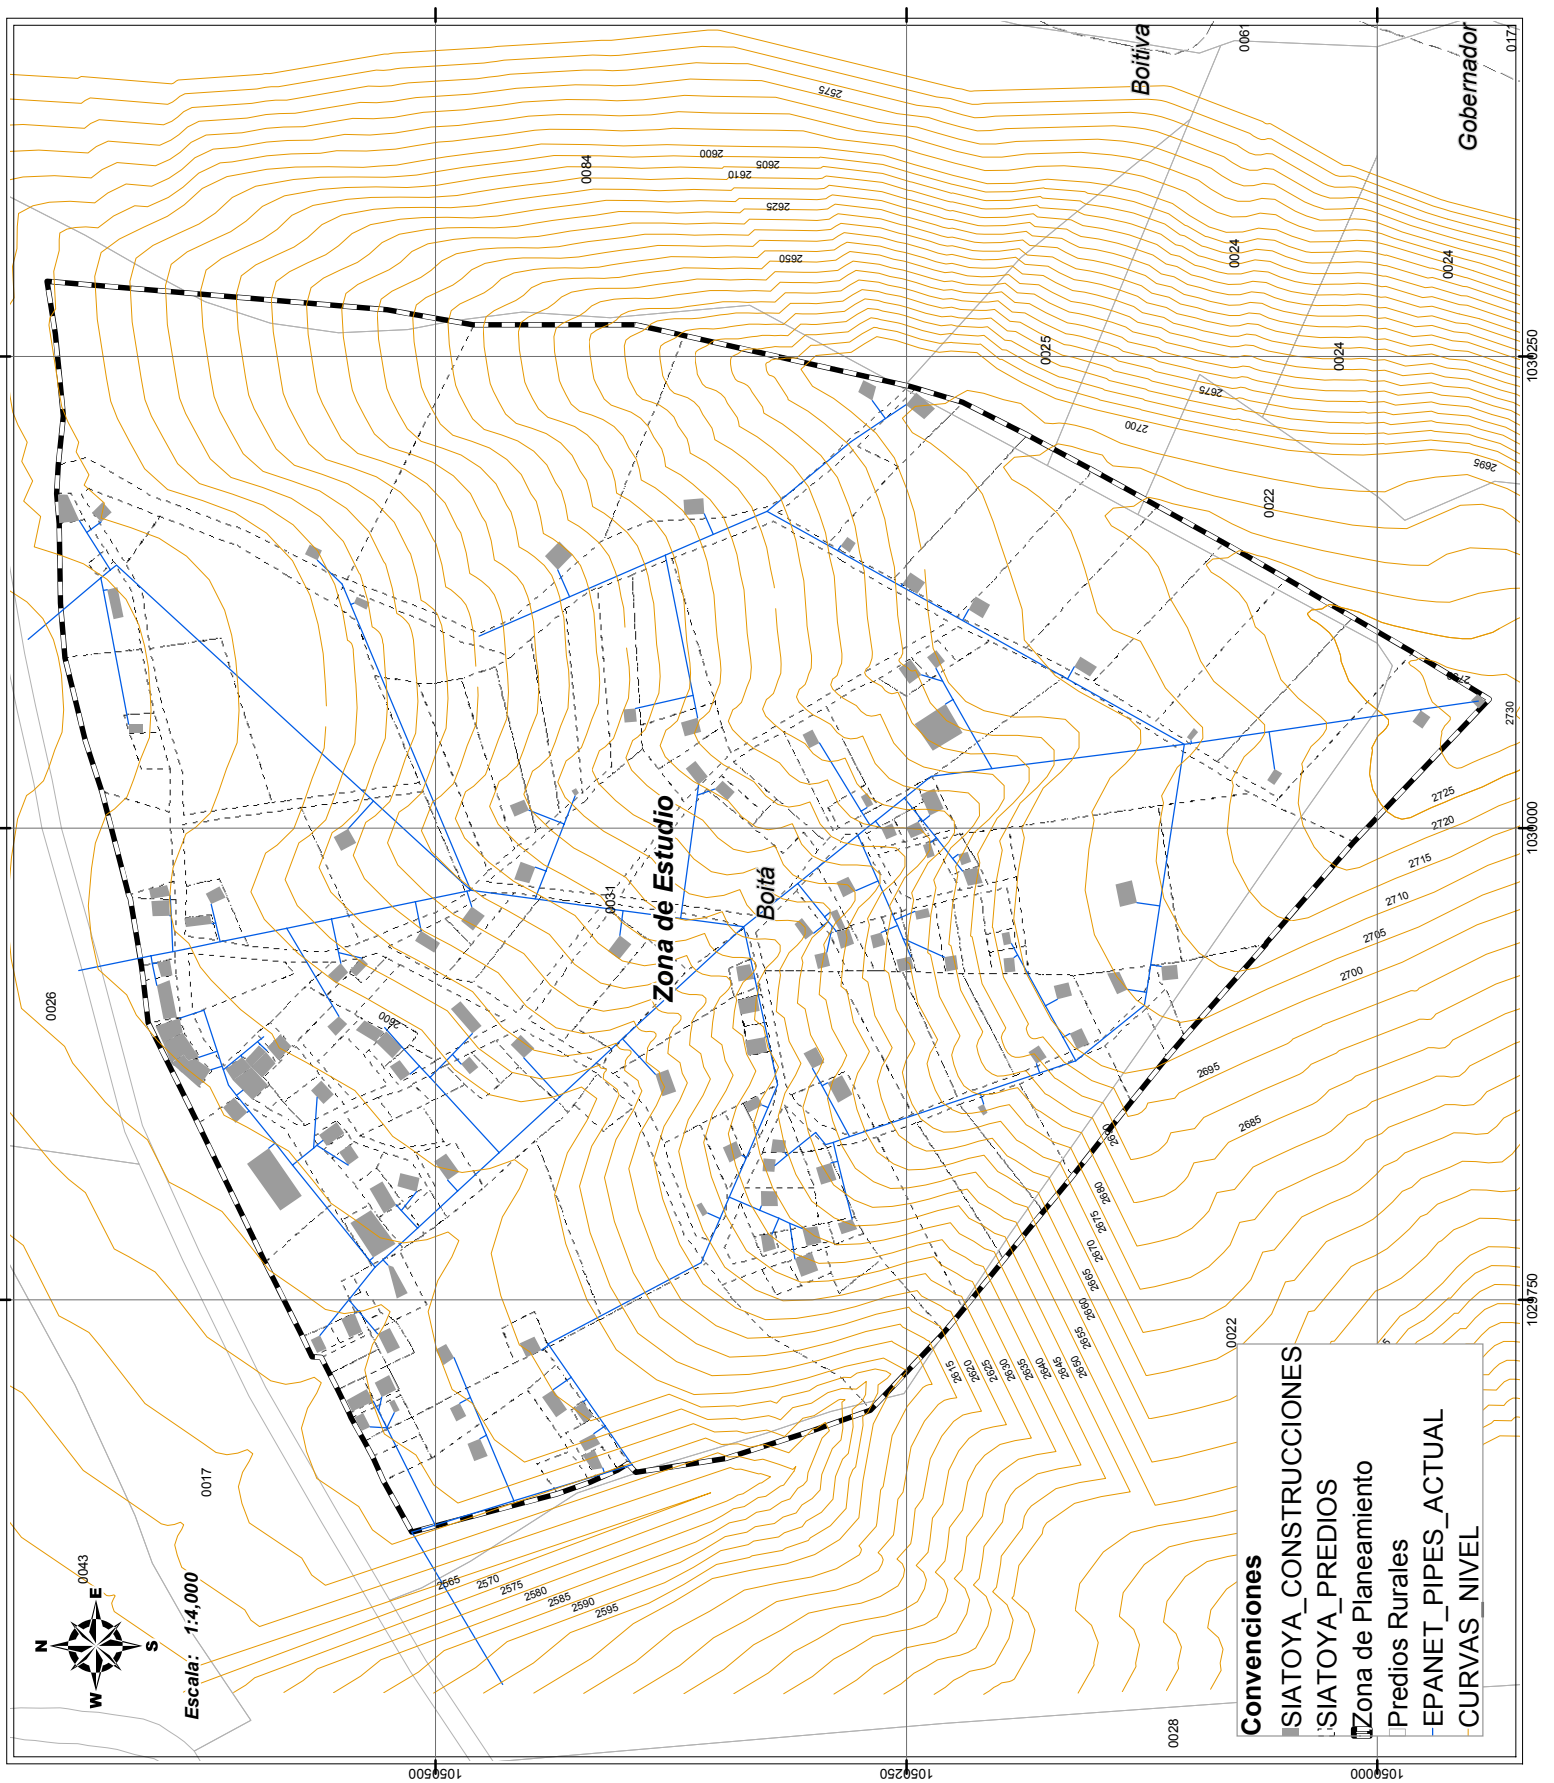

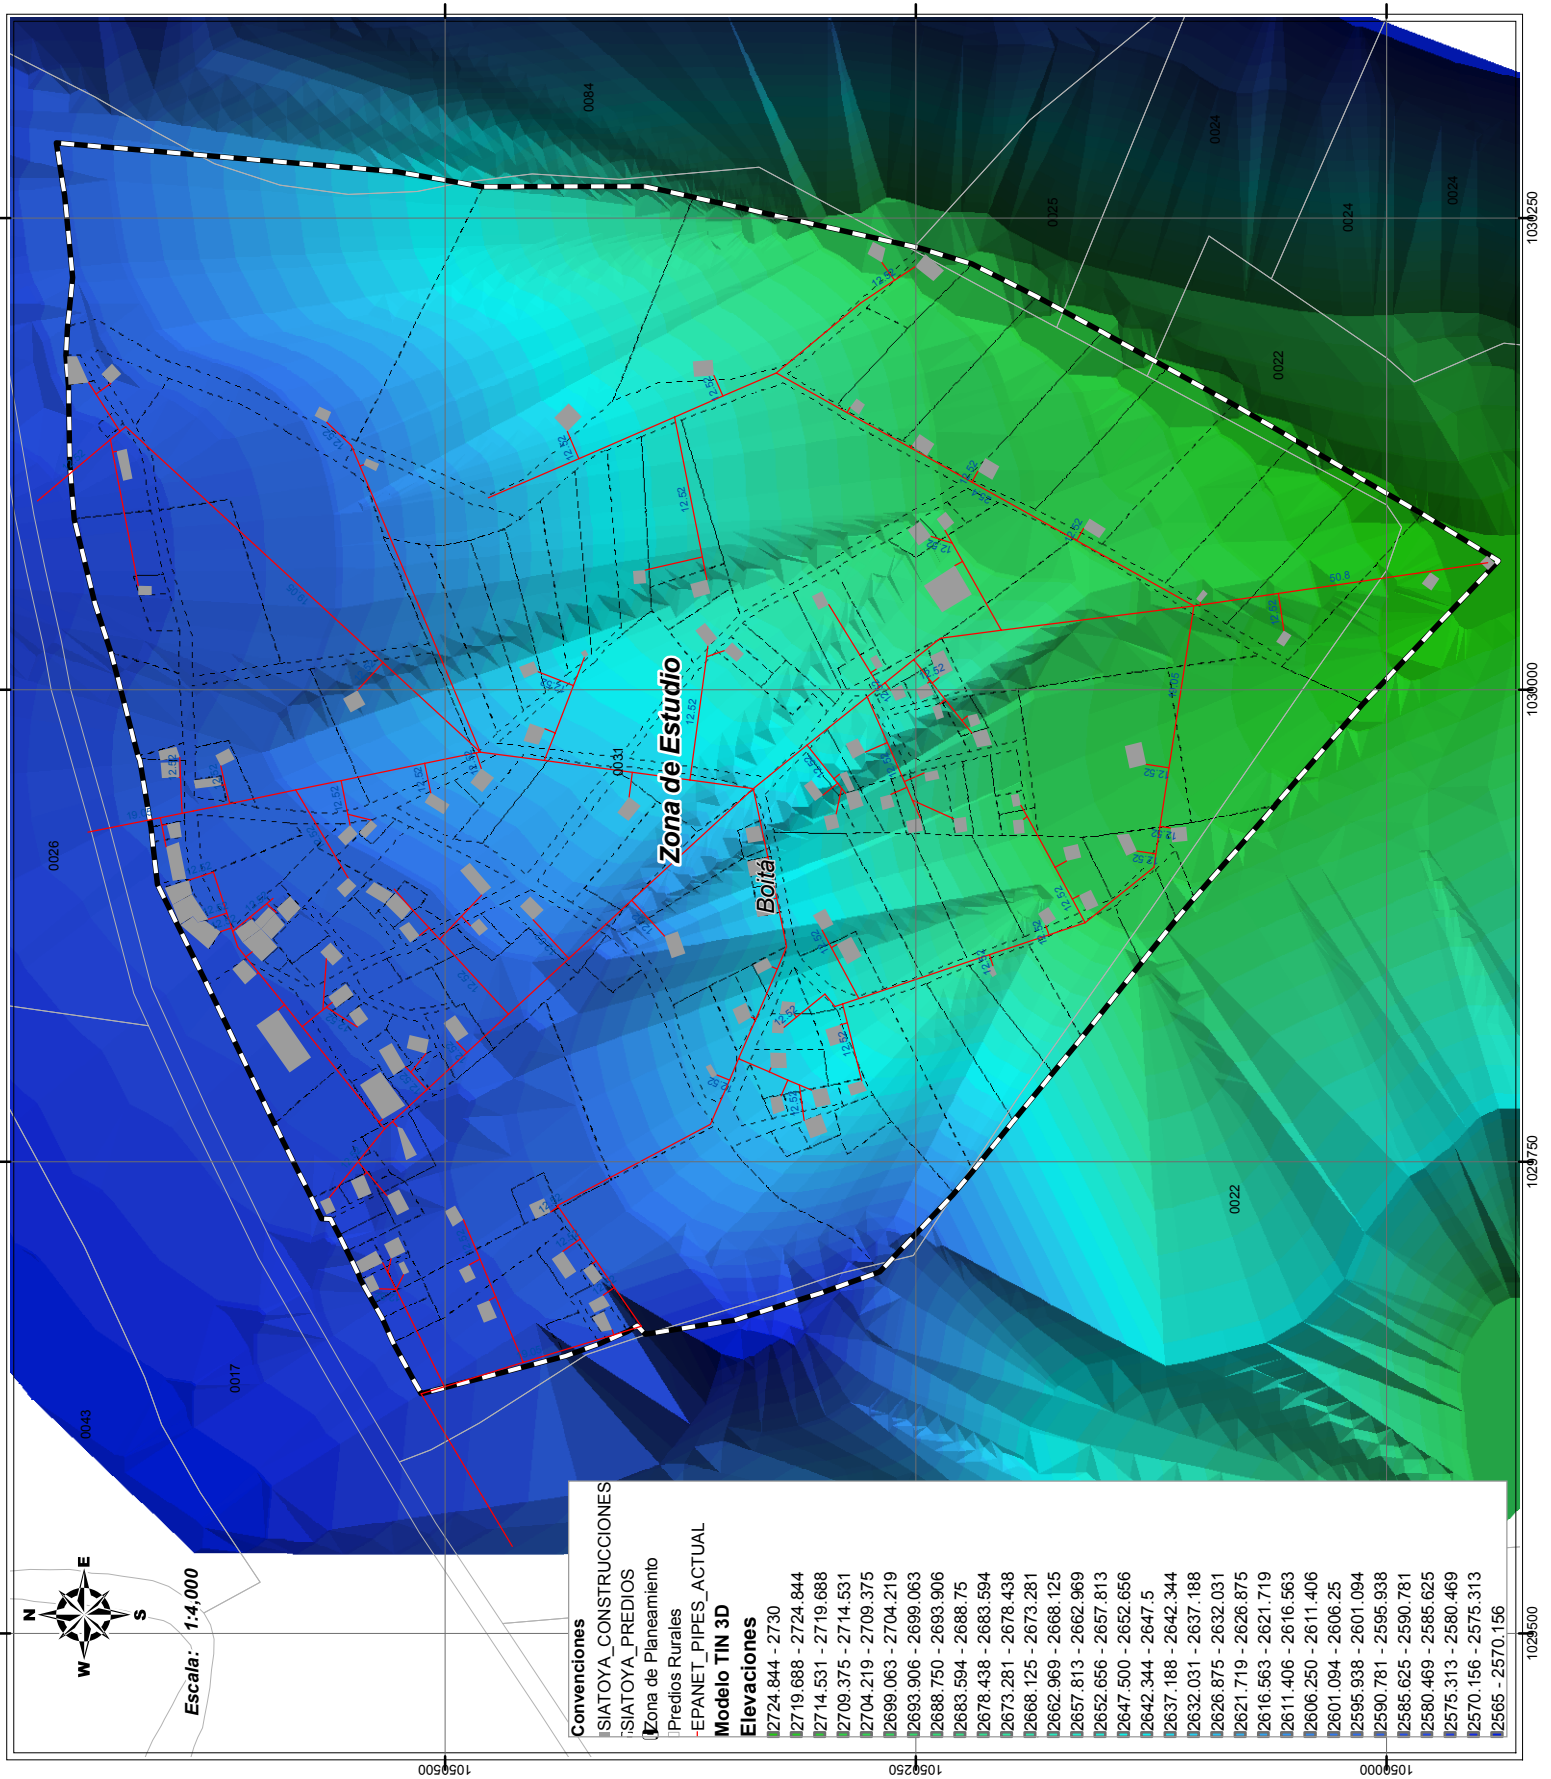

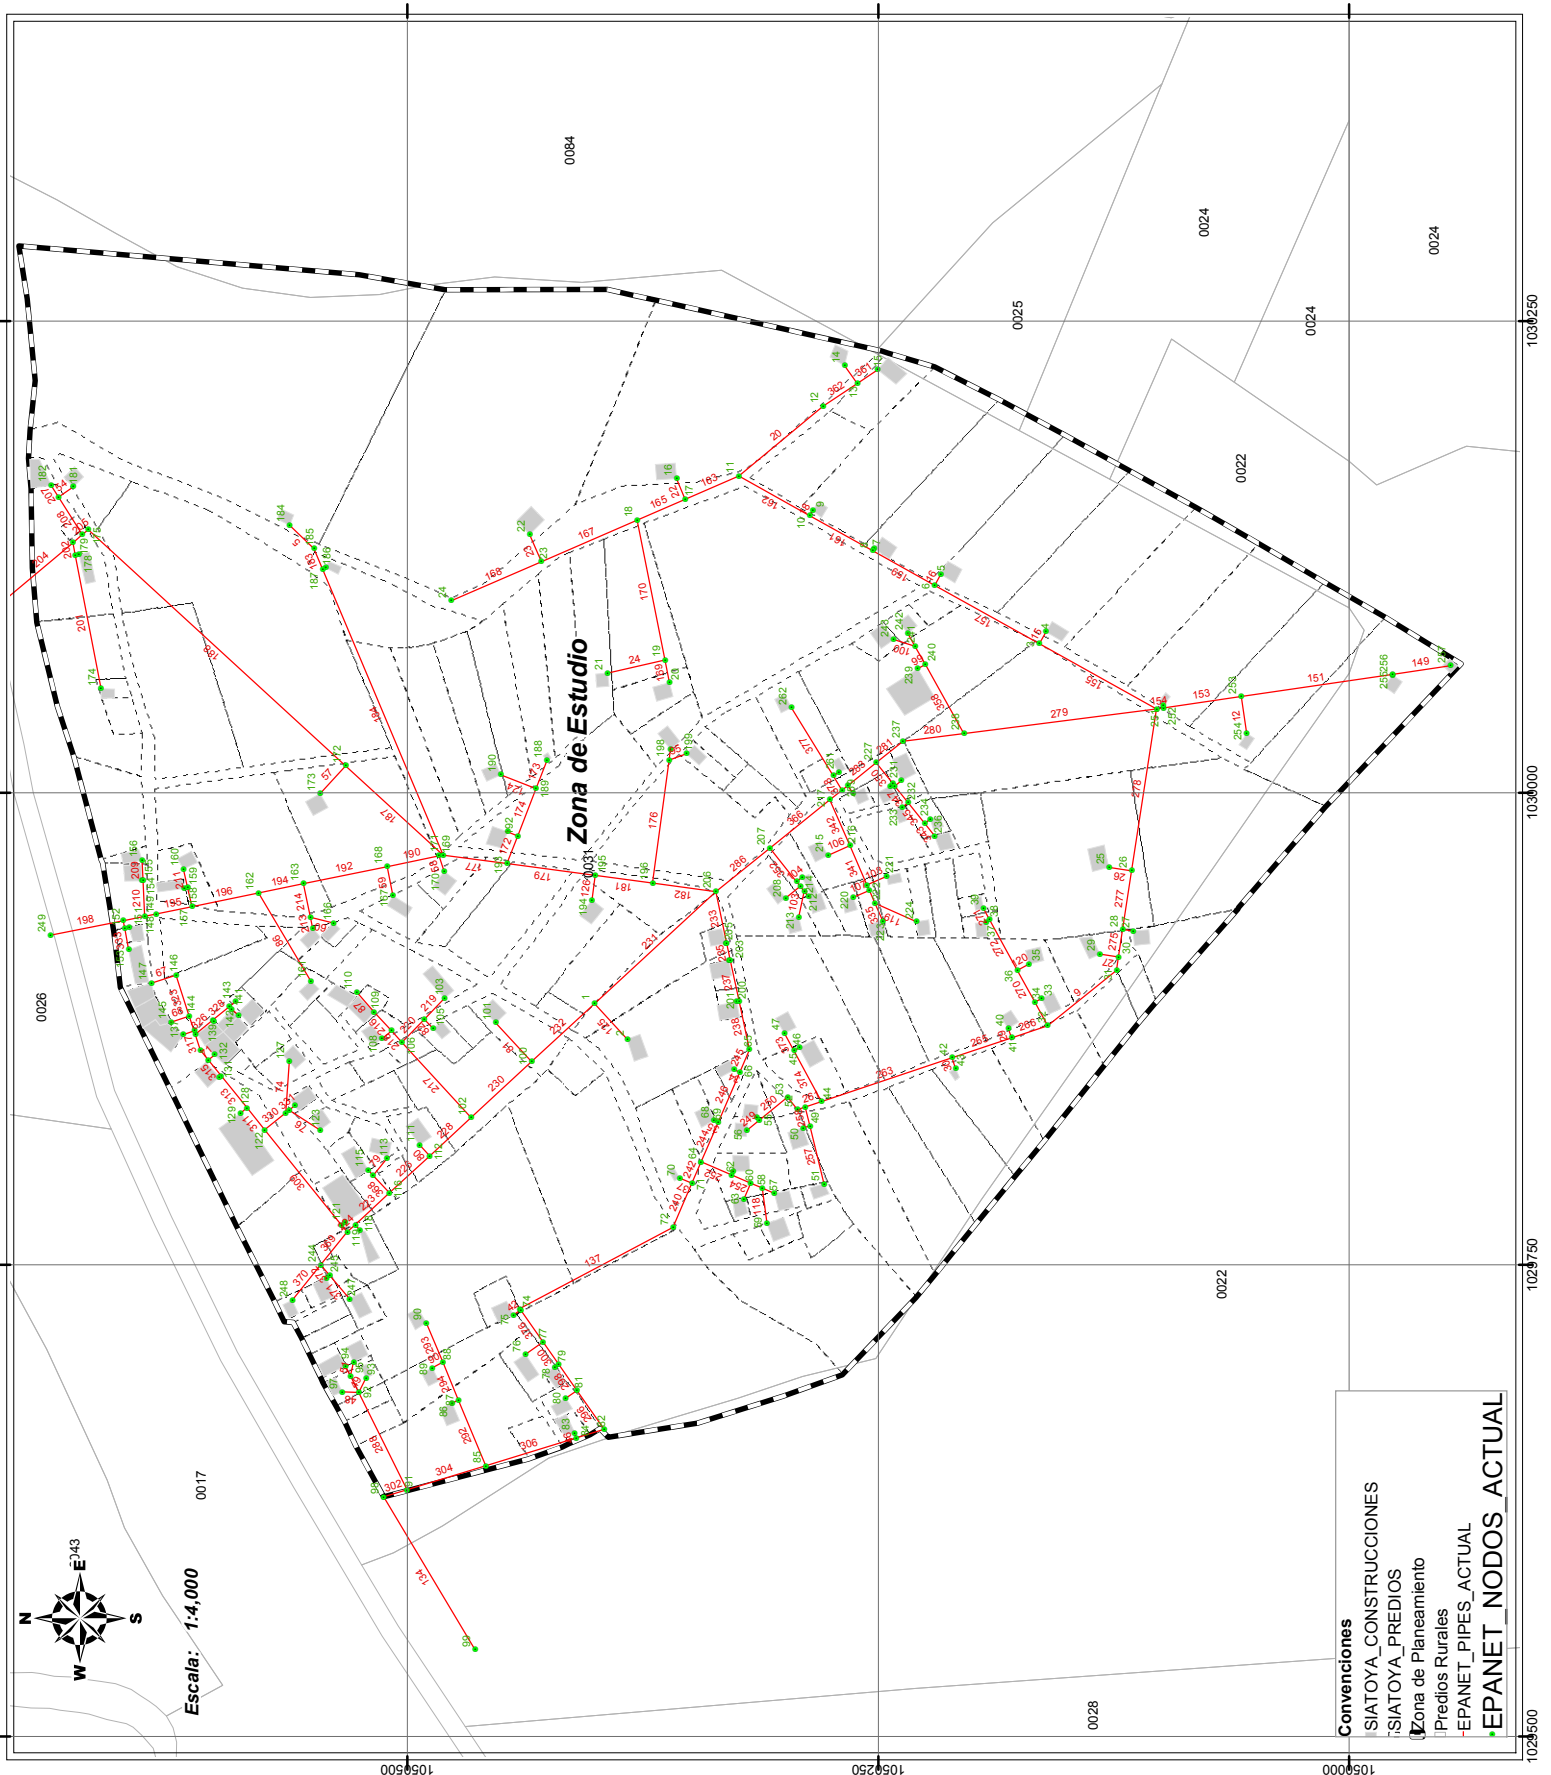

Escala: 1:4,000

Zona de Estudio

- Convenciones**
- SIATOA_CONSTRUCCIONES
 - SIATOA_PREDIOS
 - Zona de Planeamiento
 - Predios Rurales
 - EPANET_PIPES_ACTUAL
 - EPANET_NODOS_ACTUAL

